


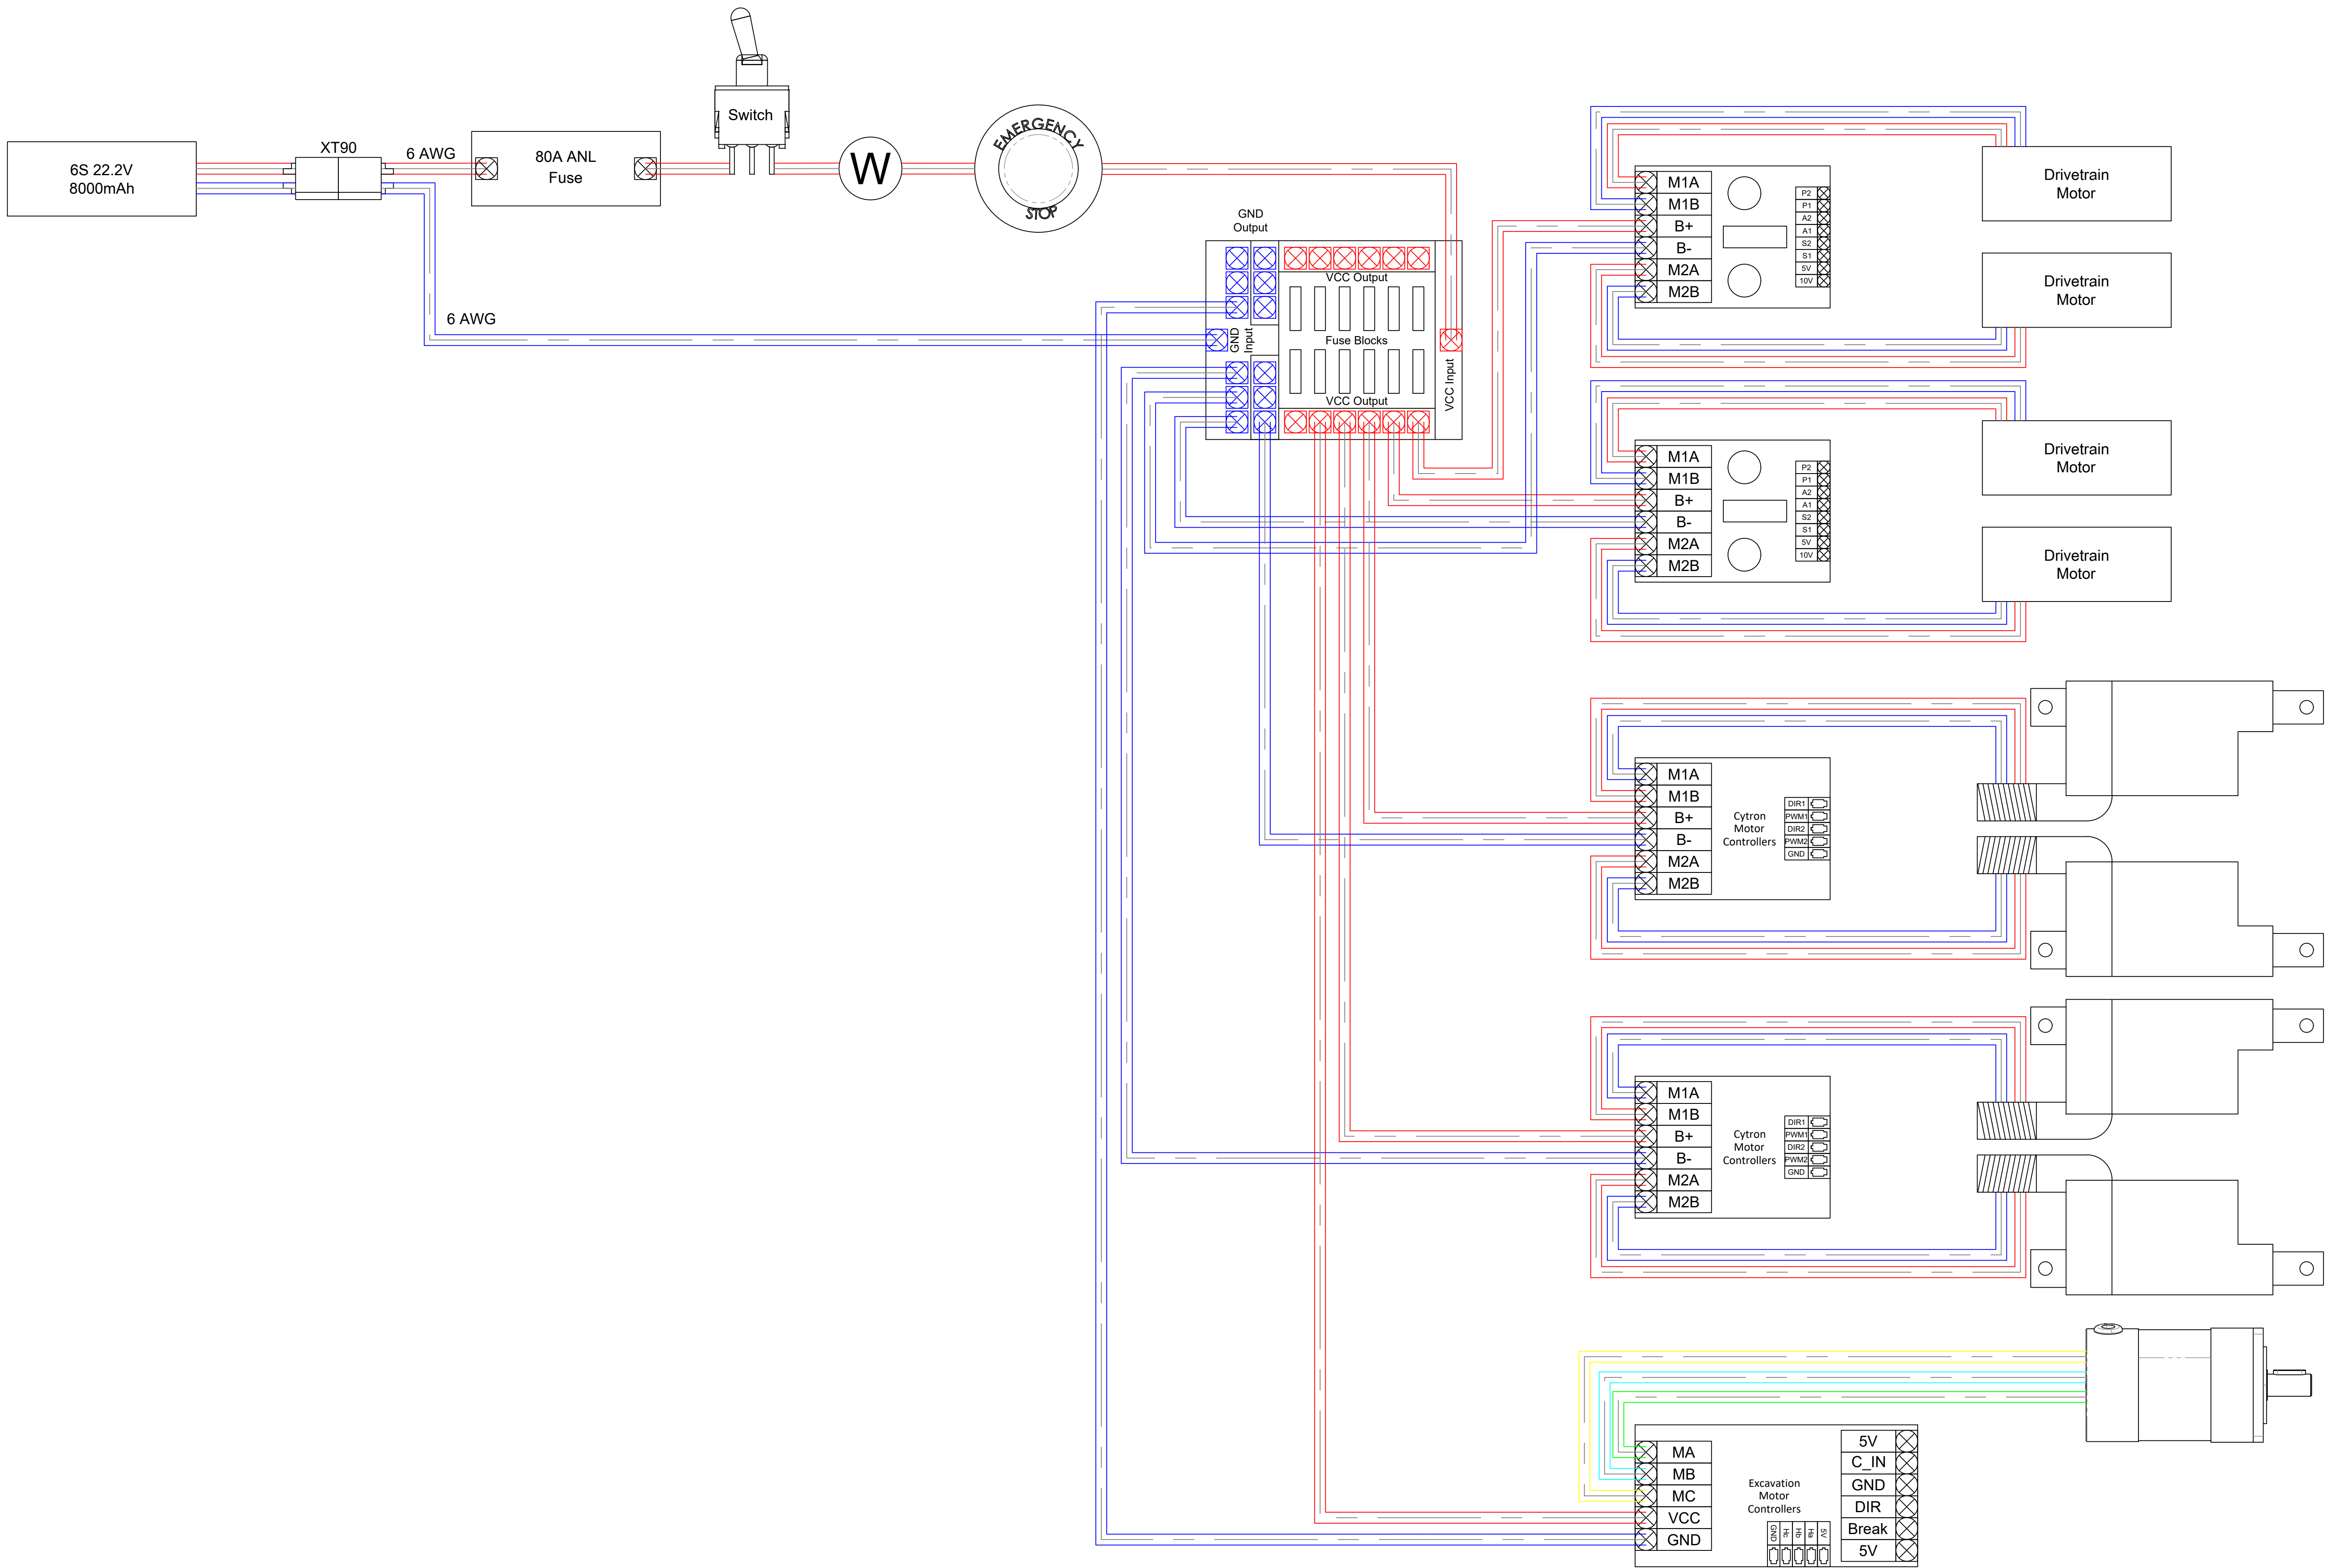

DATE	
DRAWING TITLE:	
PROJECT DESCRIPTION:	
PROJECT ADDRESS:	
DRAWN BY:	
APPLICANT(S):	
SCALE	
DRAW NO.	